


GROUND_DIMENTION LAYOUT PLAN

Scale: 1/50

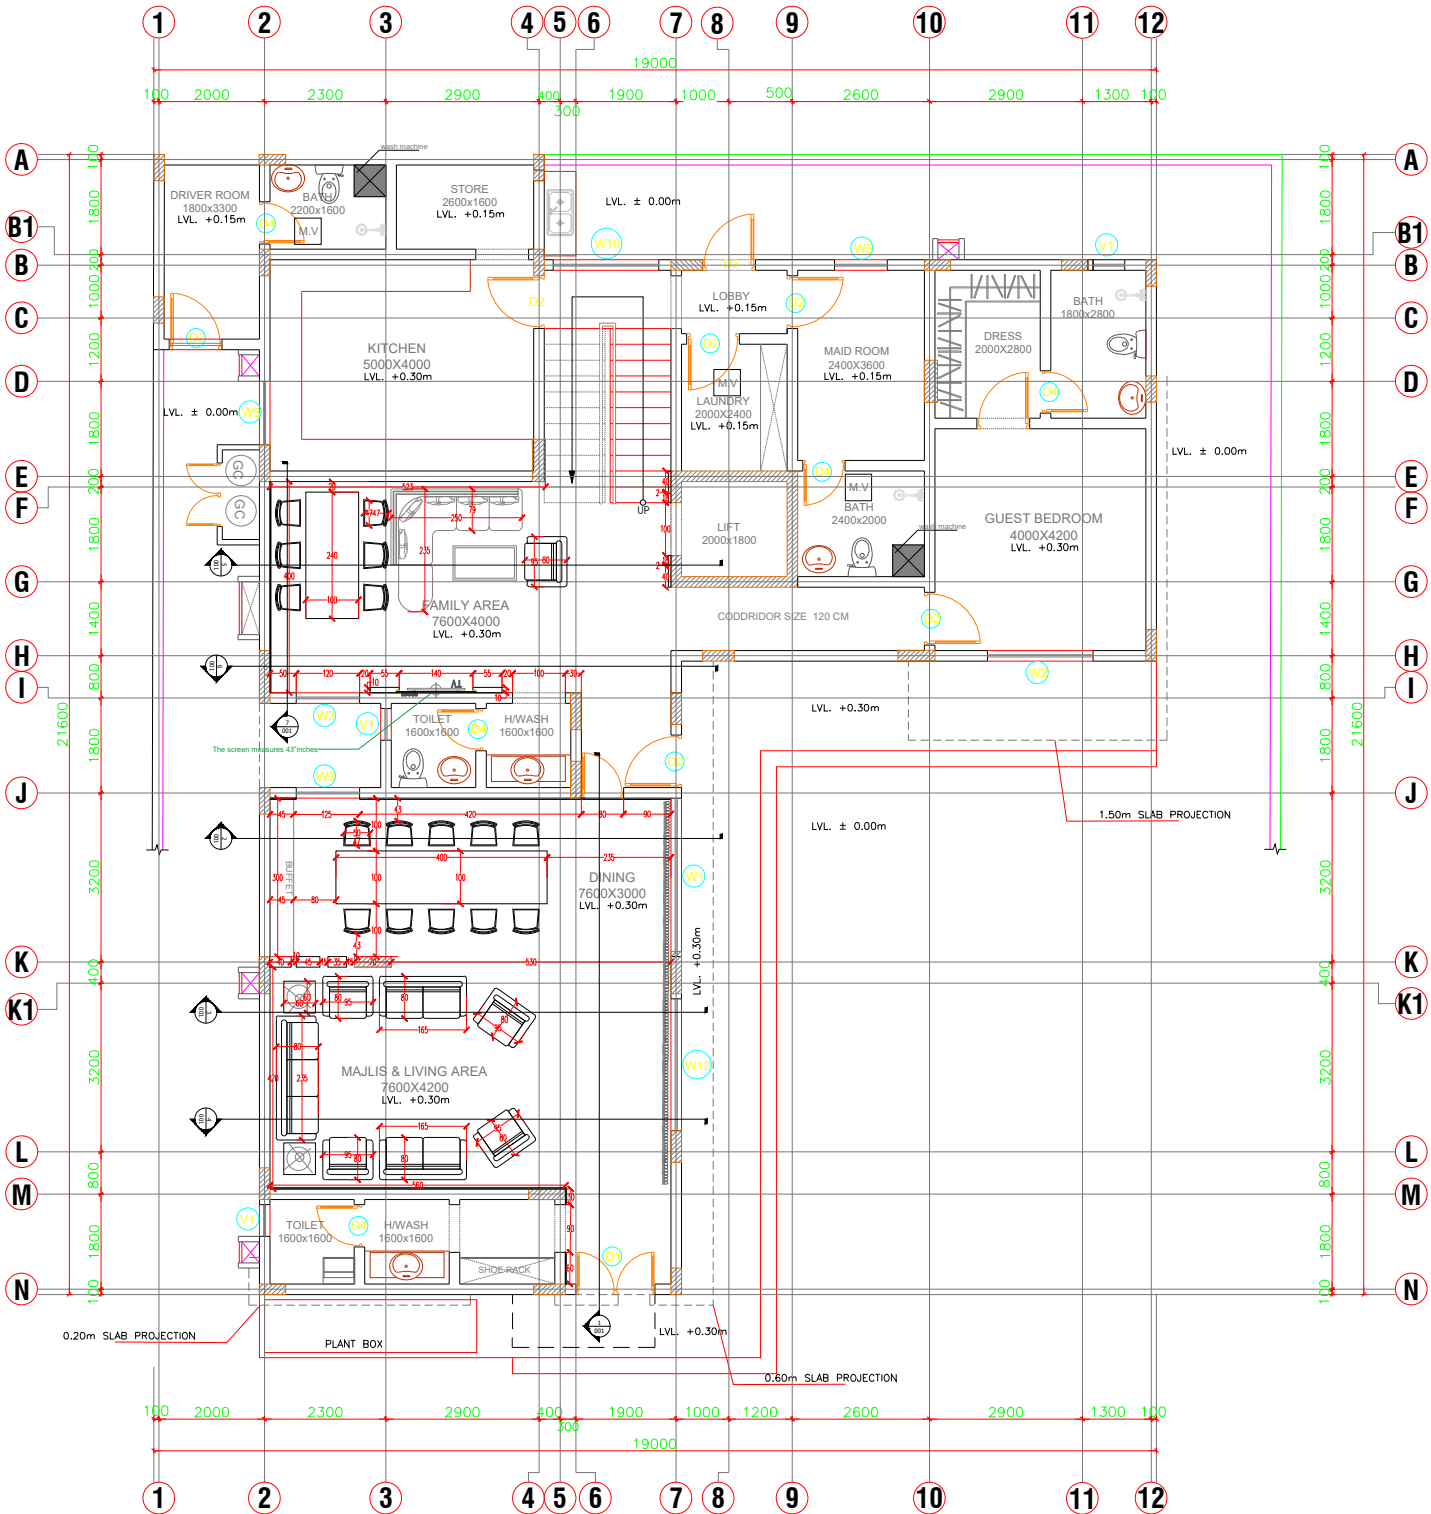

M1	acrylic rose gold \ thickness 4mm
M2	MDF CLADDING ash veneer \ thickness 20mm
M3	Jotun Paint \white comfort(8395)
M4	gypsum board cladding painted with Jotun Paint \white comfort (8395)
M5	Plastic Composite WPC PVC Wall Panels
M6	porcelain SLAP open book (As per 3d photos)
M7	Jotun decorative Paint \lady design_gray_
M8	gypsum MOLDING painted with Jotun Paint \SOFT GREY (0394)
M9	Mdf Fabric Wrapped Panel
M10	gypsum board & MOLDING painted with Jotun decorative Paint \lady design_gray_
M11	clear mirror thickness 6 mm
M12	Jotun Paint \Oxford River(9915)
M13	gypsum MOLDING painted with Jotun Paint \Oxford River(9915)
M14	FLUTED TEMPERED GLASS / V SHAPE
M15	POWDER COATED STEEL FRAME (GOLD/OR SS STEEL IF AVAILABLE)
M16	Acrylic BLACK \ thickness 4mm
M17	gypsum MOLDING painted with Jotun Paint \white comfort (8395)
M18	MDF laminated \ thickness 20mm
M19	MDF COLUMN ash veneer \ thickness 20mm
M20	fabric(As per 3d photos)
M21	Jotun Paint \space (10678)
M22	gypsum board cladding painted with Jotun Paint \preez
M23	Jotun Paint \gray color
M24	GLASS
M25	metal tube
M26	Jotun decorative Paint (Light oil color)
M27	Smooth and Glossy WPC PVC Composite Wall Panels
M28	MDF CLADDING oak veneer(WHITE COLOR) \ thickness 20mm
M29	marble SLAP open book (As per 3d photos)
M30	MDF CLADDING paint
M31	Porcelain tiles
M32	Korean slab
M33	Marble Black
M34	CNC CUT (FOREX ORNAMENT)
M35	CLEAR GLASS
M36	MDF CLADDING oak veneer(DRAK GREY COLOR) \ thickness 20mm
M37	Stone Cladding
M38	MDF cabinet veneer
M39	Travertine Beige
M40	stone sheet SLAP



PROJECT: RESIDENTIAL VILLA

LOCATION:BAWSHAR

CLIENT:
MR.HAMZA MUSTAFA MOHSIN AL LAWATI

DATE: 20-10-2025

DESIGNED BY:
ARCH.ABDULLAH HAYANI

SCALE :AS PER A3 PAPER